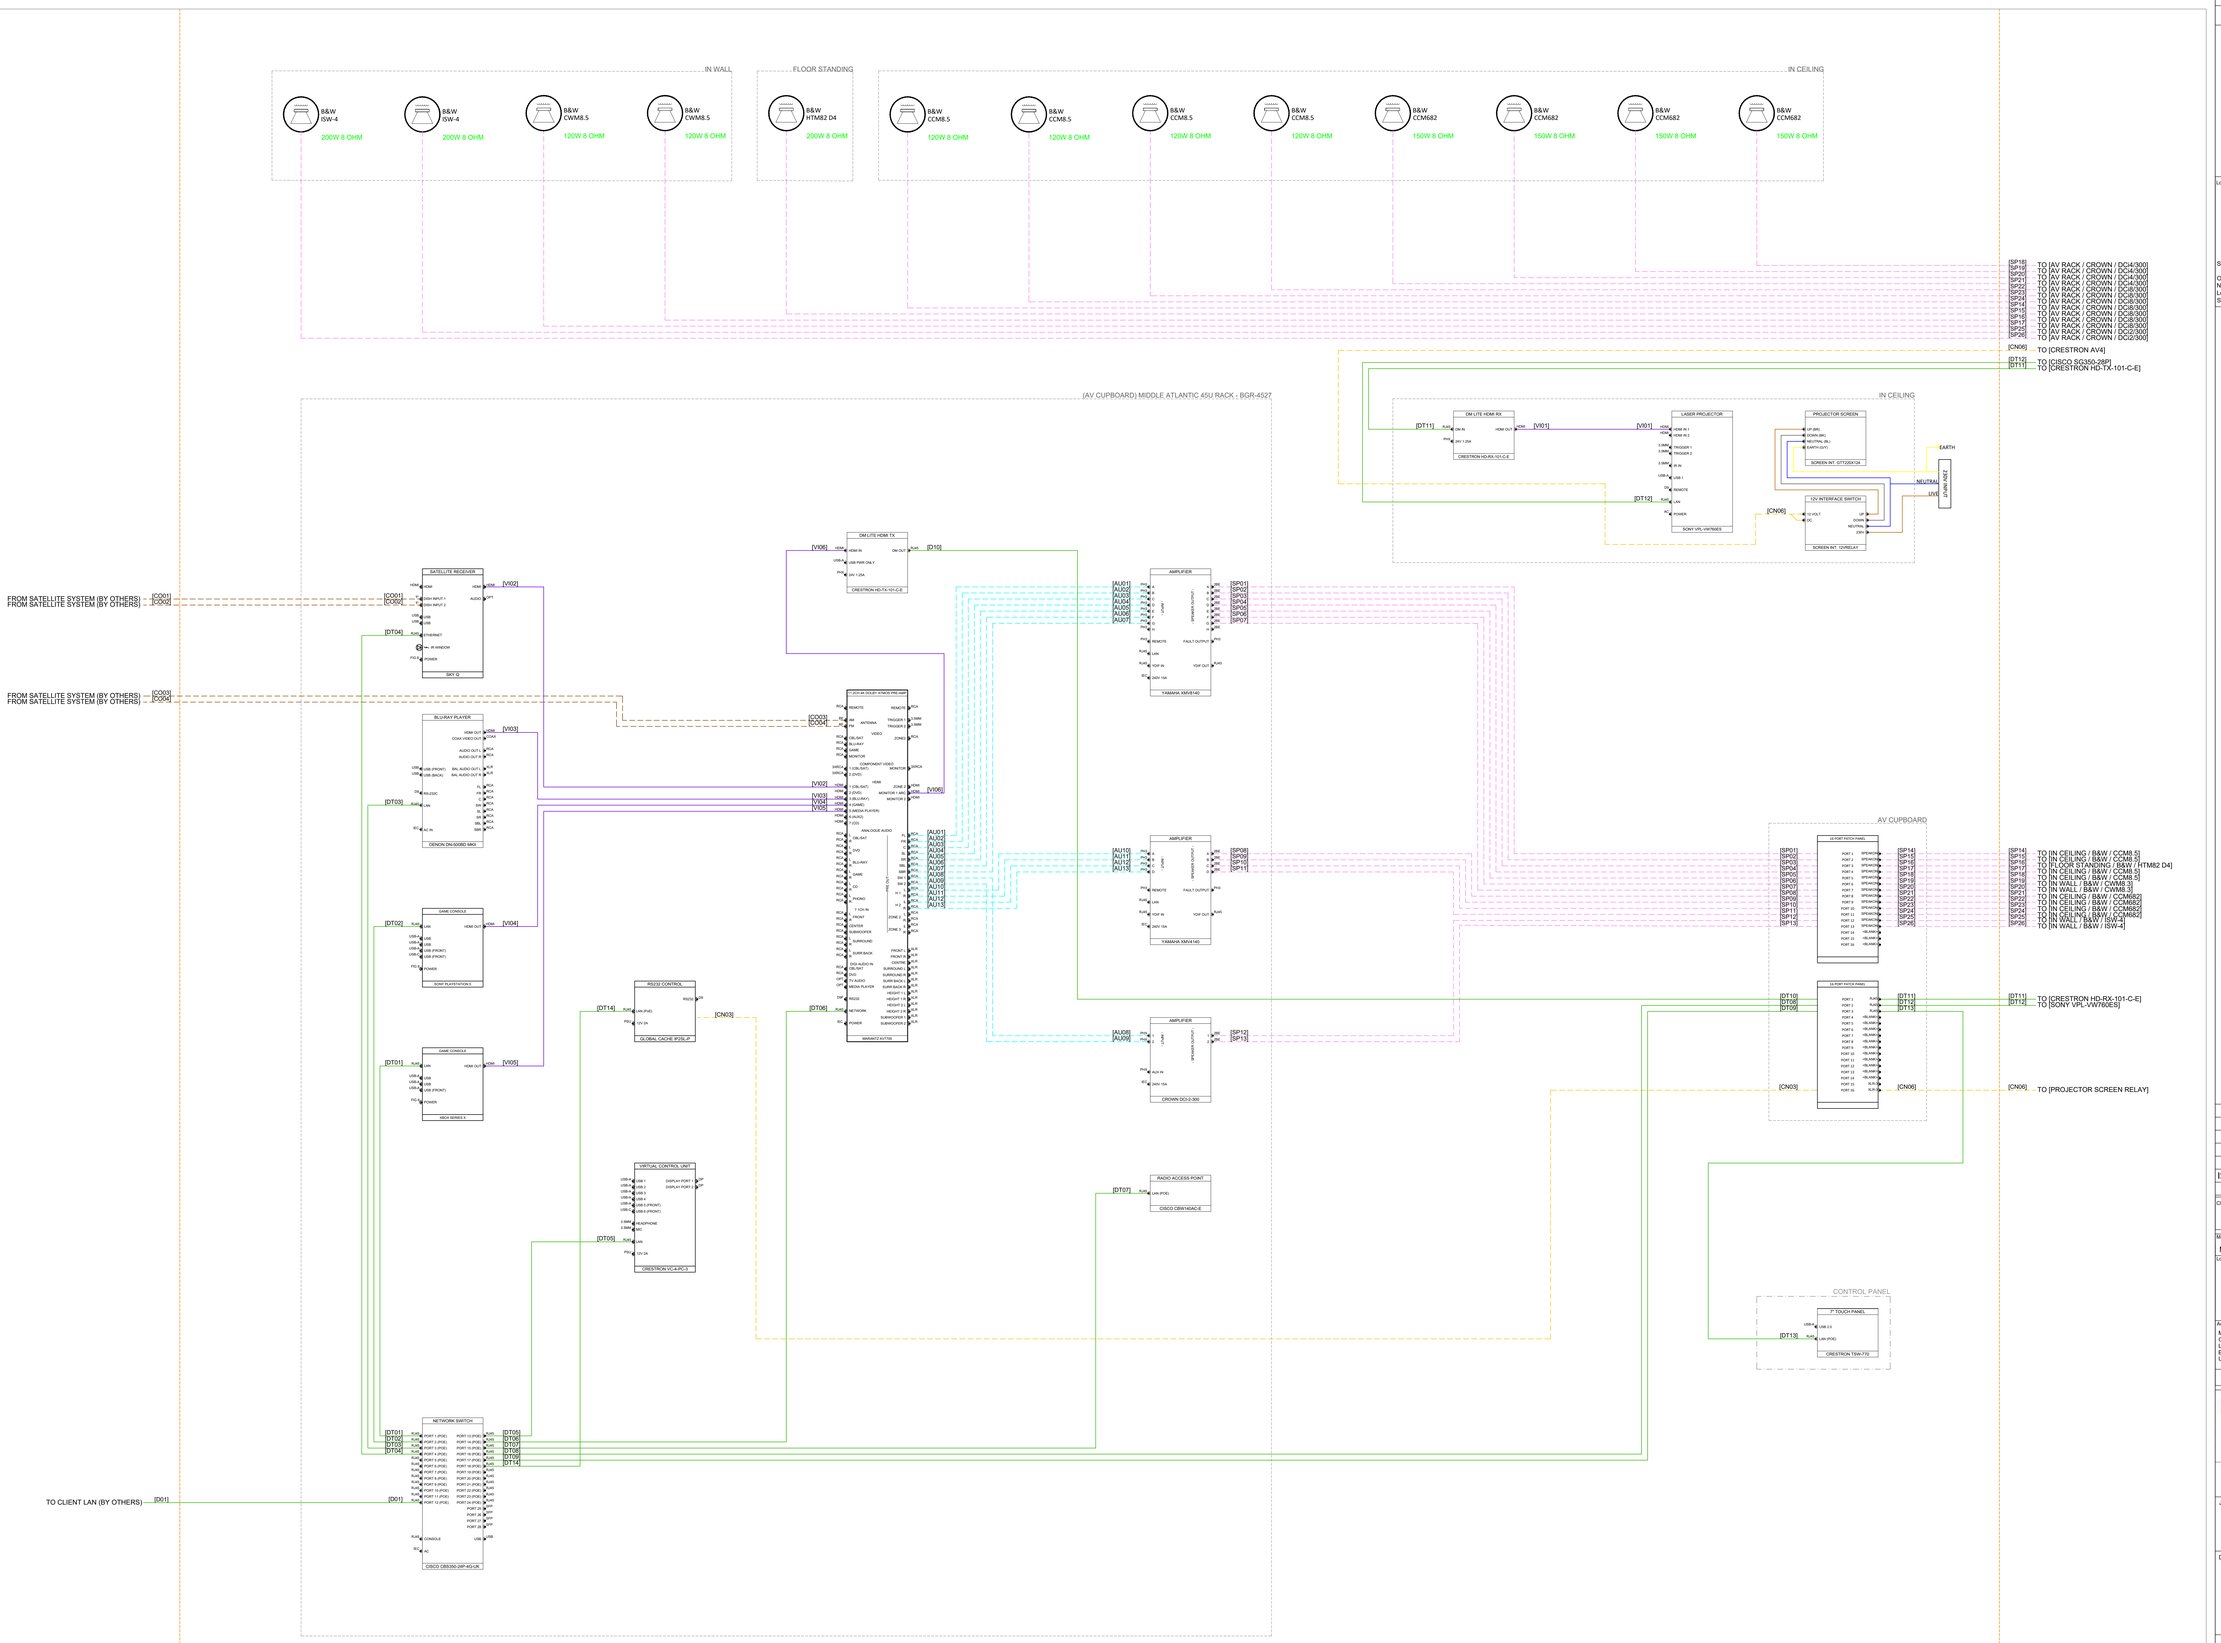

CDM REGULATIONS

HAZARDS	DATE ADDED	DATE MITIGATED	RISK ASSESSMENT DATE

Key Plan

Location Map:

Site Address:

One
Nine Elms Lane
London
SW8

Notes

1. Reference Drawing:
   SWECO 113692/SW/T/6006 Rev04
   SWECO 113692/CT/E/2701 Rev16

Legend

- Cat6 Data Cable
- WF100 Coaxial Cable
- Fibre Optic Lead

REV	DATE	ORIG	CHK'D	APP'D
00	21/04/2023	CL	DV	LF

ISSUED FOR CONSTRUCTION

Client: R&F 富力地产 R&F PROPERTIES

Main Contractor: MULTIPLEX CONSTRUCTION EUROPE LTD...

Logo: MULTIPLEX

Address:
Multiplex Construction Europe Ltd.
One Broadgate (First Floor)
London
EC2M 2QS
UK

Contact Details:
t: +44 (0) 203 829 2500
f: +44 (0) 203 829 2400
e: eulnfo@multiplex.global
w: www.multiplex.global

All drawings are in millimetres. Do not scale. This drawing is the property of Multiplex. It must not be used, copied or reproduced without permission. © Copyright Multiplex.

TClarke

45
Moorfields
London
EC2Y 9AE

t: 020 7997 7400
w: www.tclarke.co.uk
e: drawing.office@tclarke.co.uk

Job Title

ONE NINE ELMS

Drawing Title

CITY TOWER
CINEMA ROOM
LEVEL 31
AV SCHEMATIC

Scale @A0	Drawn By	Checked By	Date
N/A	CL	DV	28/04/2021

CODE & STATUS: S4 - FOR CONSTRUCTION

TClarke Job No: TC011419

Rev: 00

DRAWING No: ONE-TCL-CT-31-DR-X-65002-FO

Do not scale

© TClarke